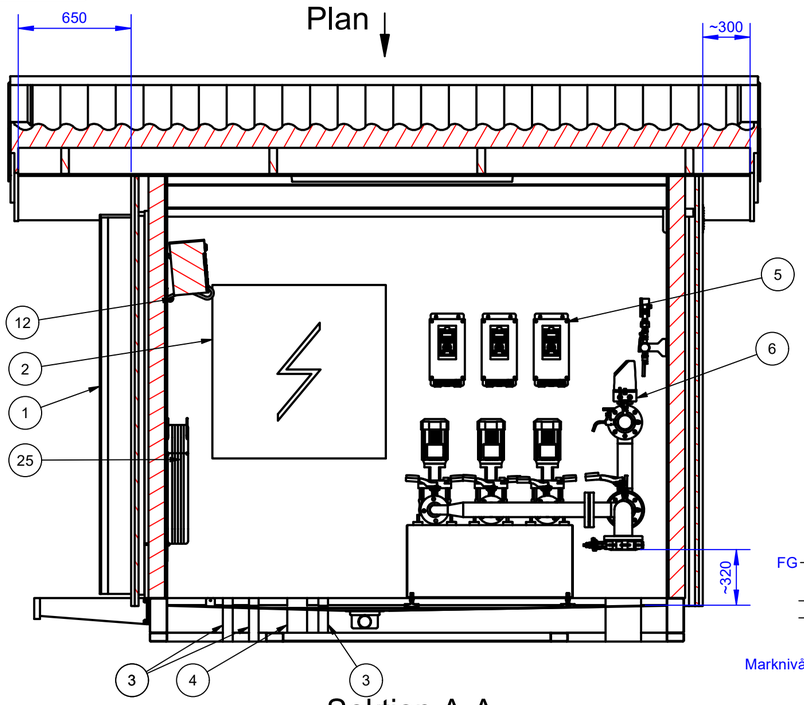

Sektion A-A

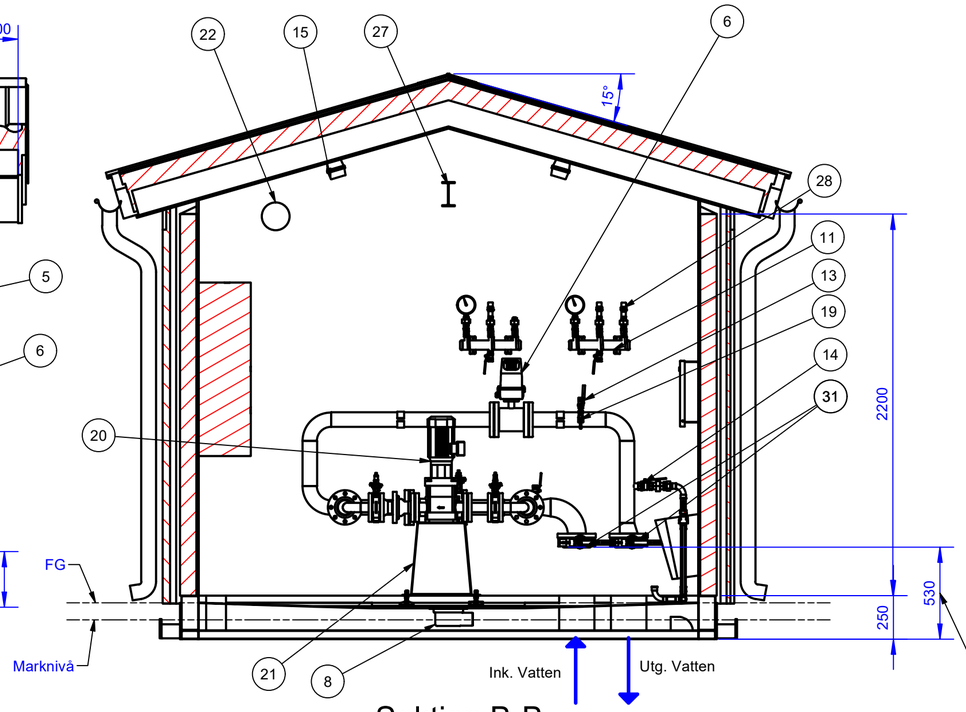

Sektion B-B

Pos	Ant	Benämning	Anteckningar
1	1	Aluminiumdörr Preconal 66 RC3	VH,10x22, Säkerhetsklass 2
2	1	Automatikskåp	BxHxD
3	3	Elgenomföring	Ø57
4	1	Elgenomföring 114.3x2.0	EN 1.4301
5	3	Frekvensomriktare	2,2KW, IP54
6	1	Flödesmätare dn80	Kompakt Siemens Magflo 5100W/5000, EPDM
7	1	Genomföring reservkraft	EN 1.4301
8	1	Golvbrunn Purus Ymer	sidoutlopp Ø75
9	1	Hydropress 100l	
10	1	Hygienutrustning	Tvättställ, Clage 3,5 kW, tvål/desinf & pappershållare
11	2	Intrumentmanifolder	manometer 0-6bar, tryckgivare, pluggat
12	1	Klädhängare	
13	10	Kulventil dn15	
14	1	Kulventil dn25	
15	2	Lysrörsarmatur 2x36w	
16	3	Membranbackventil dn50	
17	1	Membranbackventil dn80	
18	1	Papperskorg	
19	1	Provtagningskran DN15	Nålventil EN1.4301 + PTFE
20	3	Pump	
21	1	Pumpstativ	EN 1.4301
22	2	Självdragsventilation Ø125	
23	1	Skrapgaller	
24	1	Skrivpulpet	SP2018
25	1	Slanghylla	Inkl. 5m slang dn25
26	1	Säkerhetsventil dn15	
27	1	Telferbalk VFZ	IPE 140, 500kg
28	3	Tryckgivare dn15	
29	6	Vridspjällventil dn50	
30	1	Vridspjällventil dn80	
31	2	Vridspjällventil dn100	
32	1	Värmefläkt	2 kW

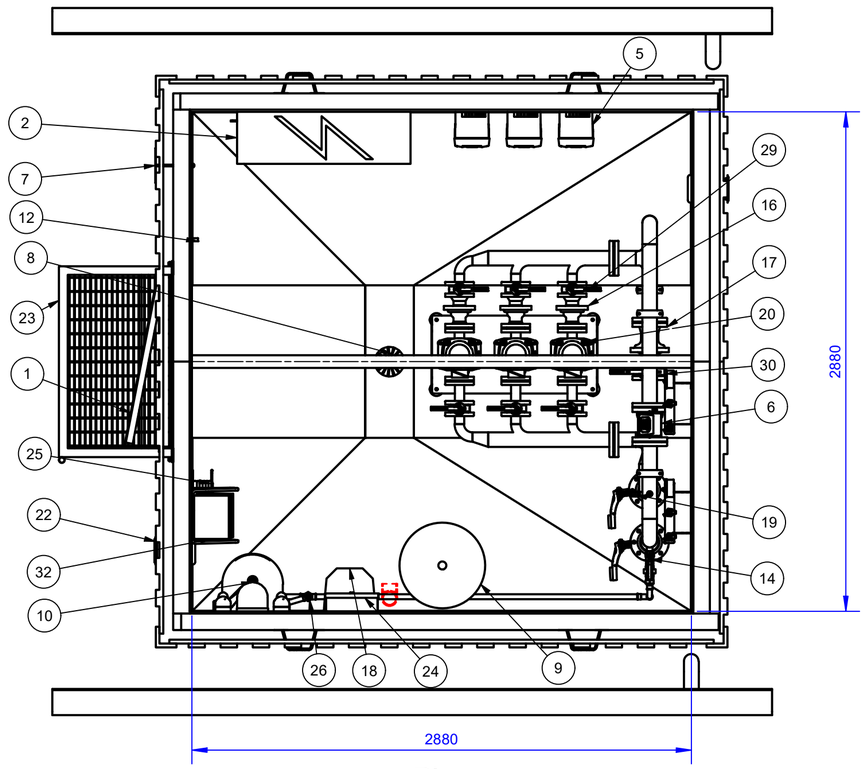

Plan

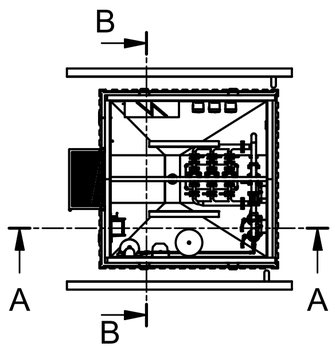

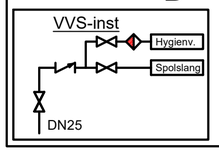

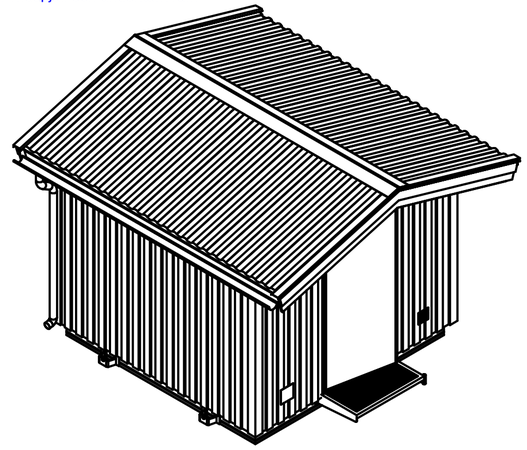

UTFÖRANDE BYGGNAD

> Fasad: Lockpanel av fibercement, Kulör
> Innerväggar: Förstärkta innerväggar för SSF2.
Med dekorvalsad rostfri plåt.
> Yttertak: Svart tegelprofilerad plåt
> Takavvattning: Svart
> Dörr: Preconal aluminiumdörr 10x22 RC3

med trycke lås och dörrbroms.

> Isolering: 95 mm i väggar & 95 mm i tak
> Ventilation självdrag: 125 mm tallriksventiler & galler

BYGGHANDLING

ROSTFRIA VA-SYSTEM
Uniwater

Projekt	Ritad av	Handläggare
Datum	Ansvarig	Granskad av

Rostfria VA-system AB
Tryckstegringsstation
Originalformat A2

Skala	Nummer	Rev
1 : 25		A

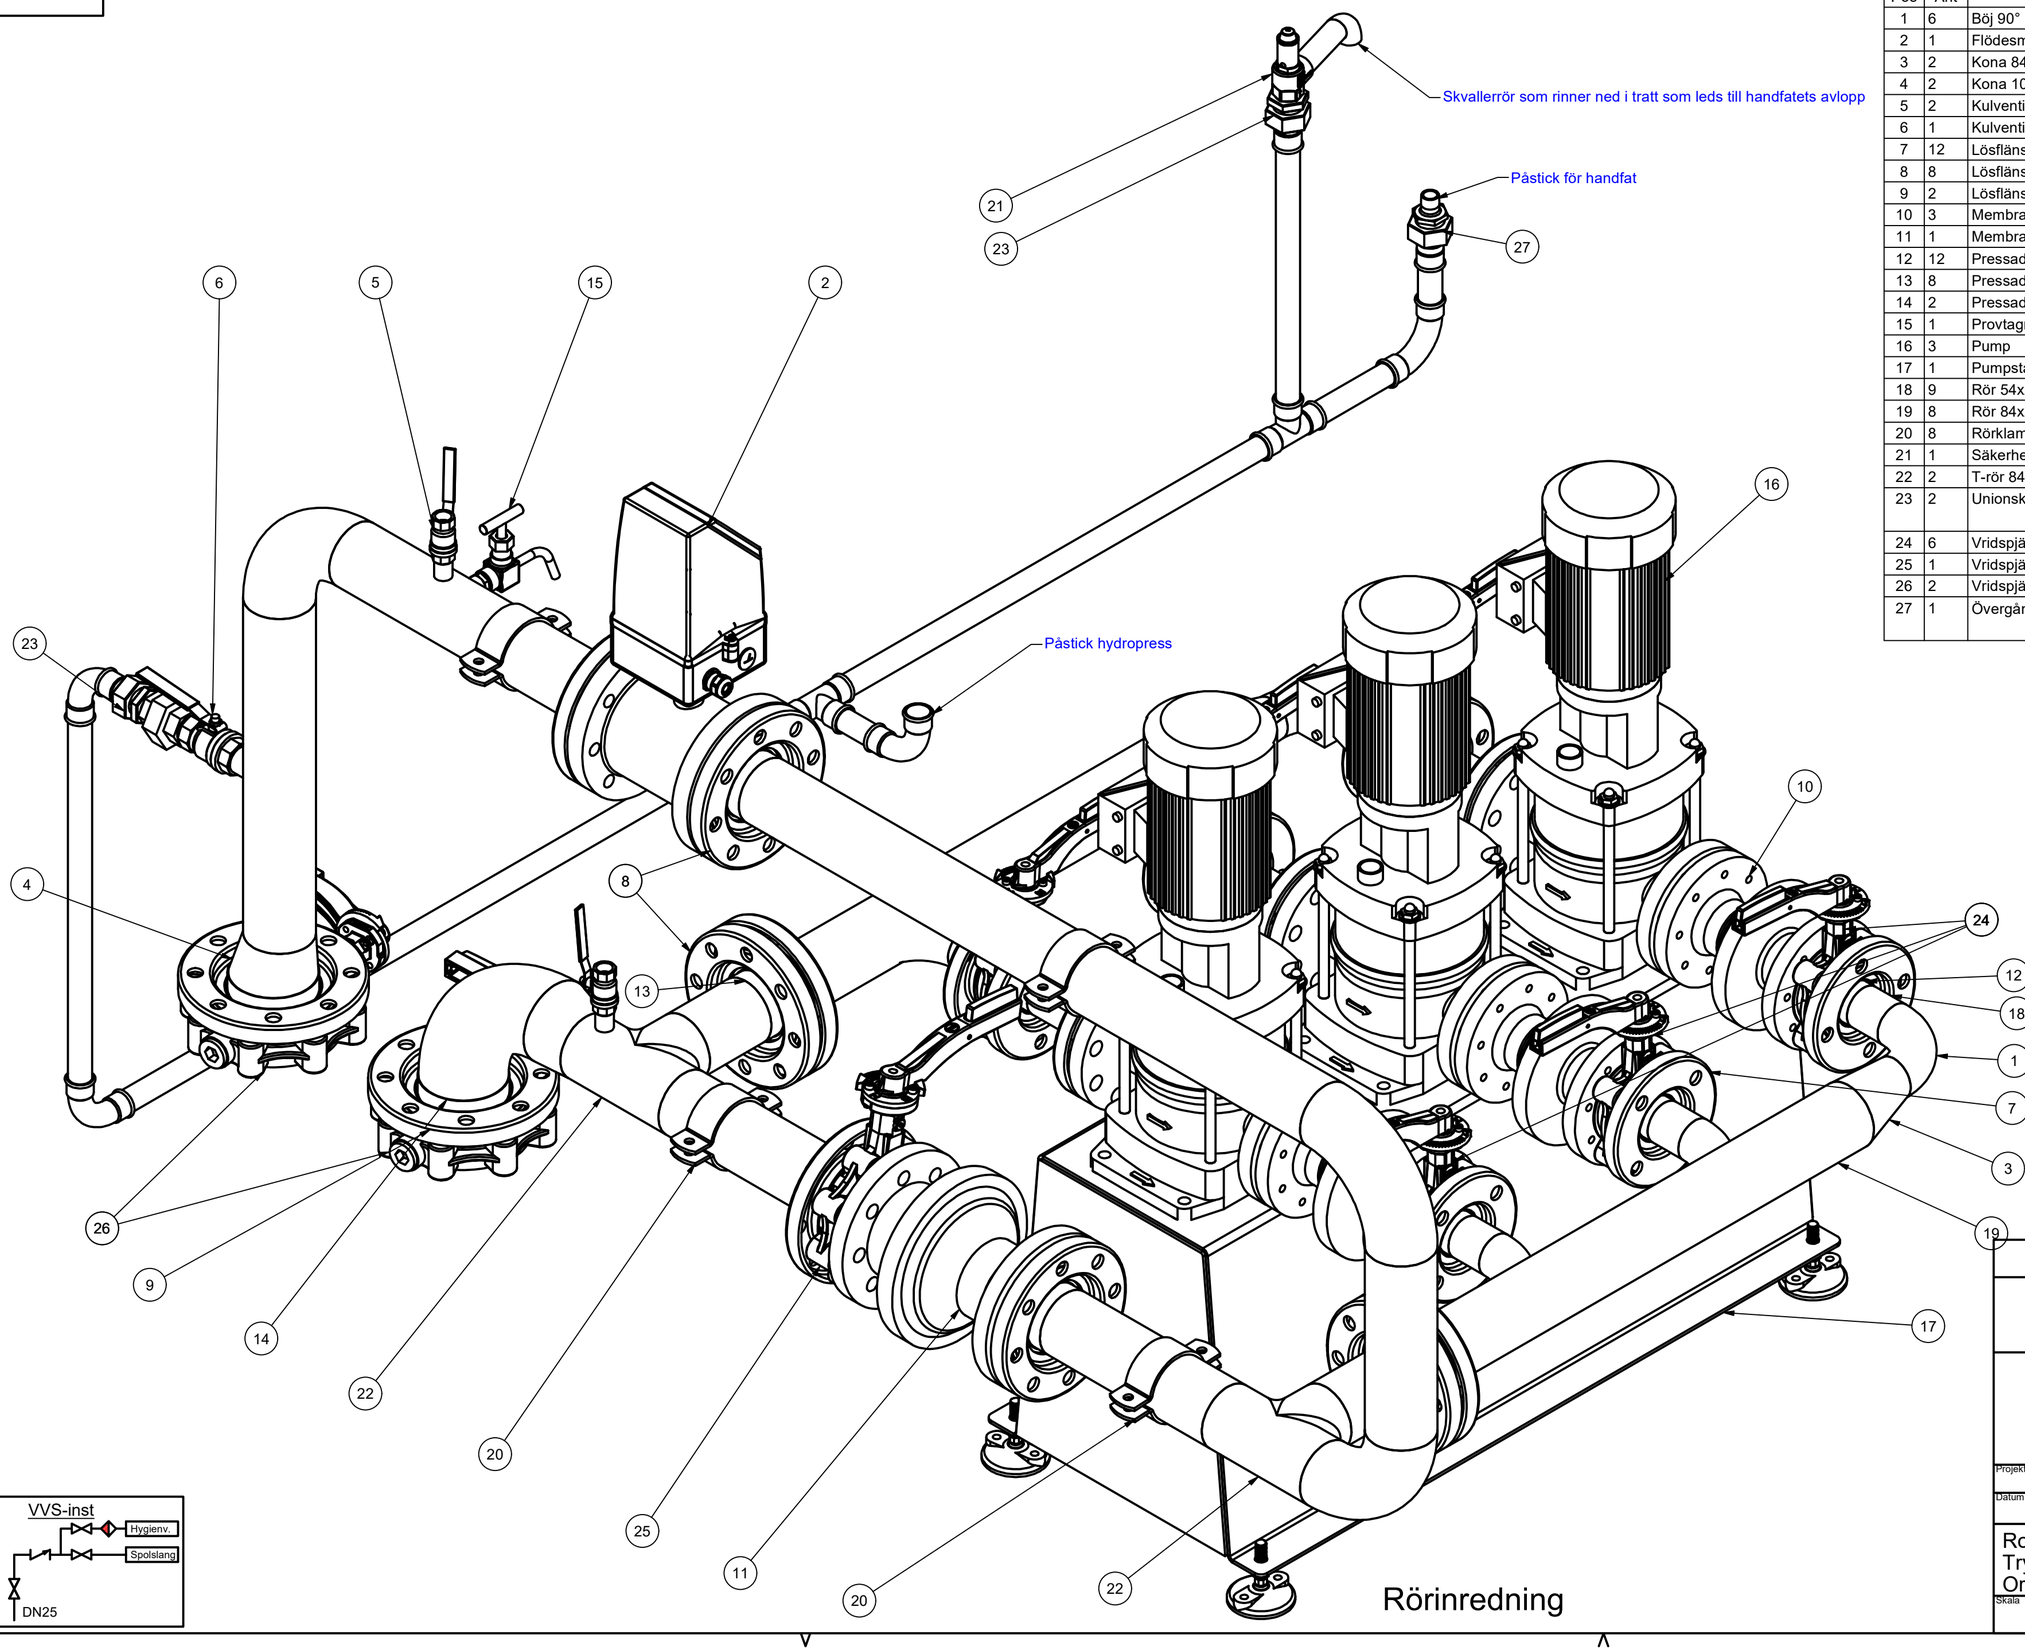

Pos	Ant	Benämning	Anteckningar
1	6	Böj 90° 54x2,0 1,5xD	Rostfritt
2	1	Flödesmätare dn80	Siemens Magflo 5100W/5000
3	2	Kona 84/54x2,0 excentrisk	Syrafast
4	2	Kona 104/84x2,0 excentrisk	Syrafast
5	2	Kulventil dn15	
6	1	Kulventil dn25	
7	12	Lösfläns dn50	EN 1.4301
8	8	Lösfläns dn80	EN 1.4301
9	2	Lösfläns dn100	EN 1.4301
10	3	Membranbackventil dn50	
11	1	Membranbackventil dn80	
12	12	Pressad krage dn50	EN 1.4432
13	8	Pressad krage dn80	EN 1.4432
14	2	Pressad krage dn100	EN 1.4432
15	1	Provtagningskran DN15	Nålventil EN1.4301 + PTFE
16	3	Pump	
17	1	Pumpstativ	EN 1.4301, med maskinfötter
18	9	Rör 54x2.0	EN 1.4301
19	8	Rör 84x2.0	EN 1.4301
20	8	Rörklammer SSG	DK84 EN 1.4301
21	1	Säkerhetsventil dn15	
22	2	T-rör 84x2,0	Rostfritt
23	2	Unionskoppling	Syrafast. Utvändig gänga 1" till pressrör 28mm.
24	6	Vridspjällventil dn50	
25	1	Vridspjällventil dn80	
26	2	Vridspjällventil dn100	
27	1	Övergångsmuff	Syrafast. Invändig gänga 1" till pressrör 28mm.

BYGGHANDLING

ROSTFRIA VA-SYSTEM Uniwater

Projekt	Ritad av	Handläggare
Datum	Ansvarig	Granskad av

Rostfria VA-system AB
Tryckstegringsstation
Originalformat A2

Skala	Nummer	Rev
1 :5		A

Rörinredning